


SITE ANALYSIS

Base: the site plan provided in the project handout (p.4), unaltered, shown in light grey. Highlights are overlays.

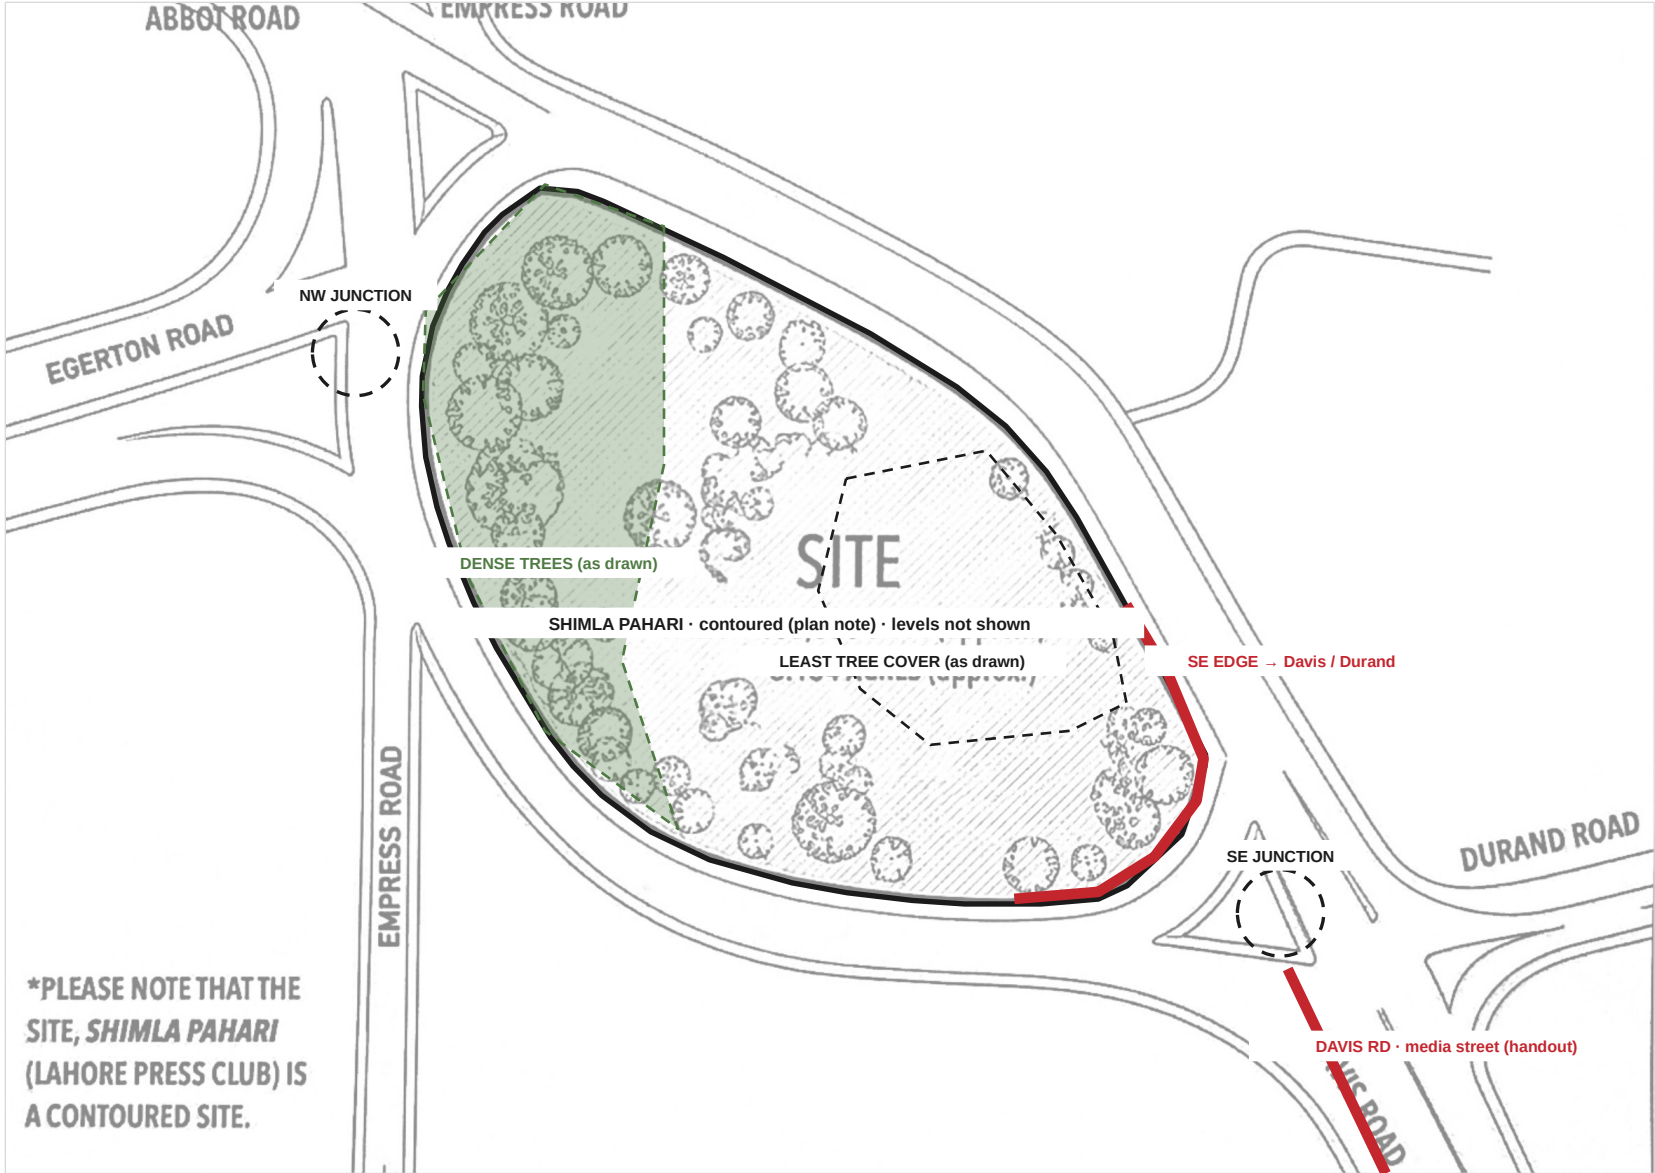

IDENTIFIED ON THE PLAN

- Boundary** ≈136,530 sq ft · 3.134 ac, oval island
- Roads** Empress · Egerton · Abbot (NW) · Davis · Durand (SE)
- Junctions** two, one at each tip, with traffic islands
- Trees** dense at W end + perimeter; least cover centre-east

NOT IDENTIFIABLE FROM PROVIDED SITE PLAN

- Press Club** no footprint or entrances drawn
- Contours** site noted as contoured, no levels
- Existing access** no gates / paths drawn
- North · scale** not shown
- Views · noise · protest spot** not shown
- Names of the two long-side roads** not labelled


FROM THE HANDOUT (TEXT)

- Davis Rd** historically a media street
- Mound** artificial, brick-kiln origin
- Rule** topography not to be altered

- site boundary
- SE public edge / Davis Rd
- dense trees (as drawn)
- - least tree cover (as drawn)
- road junction

OPPORTUNITIES + CONSTRAINTS

What the drawn site offers, and what limits it.

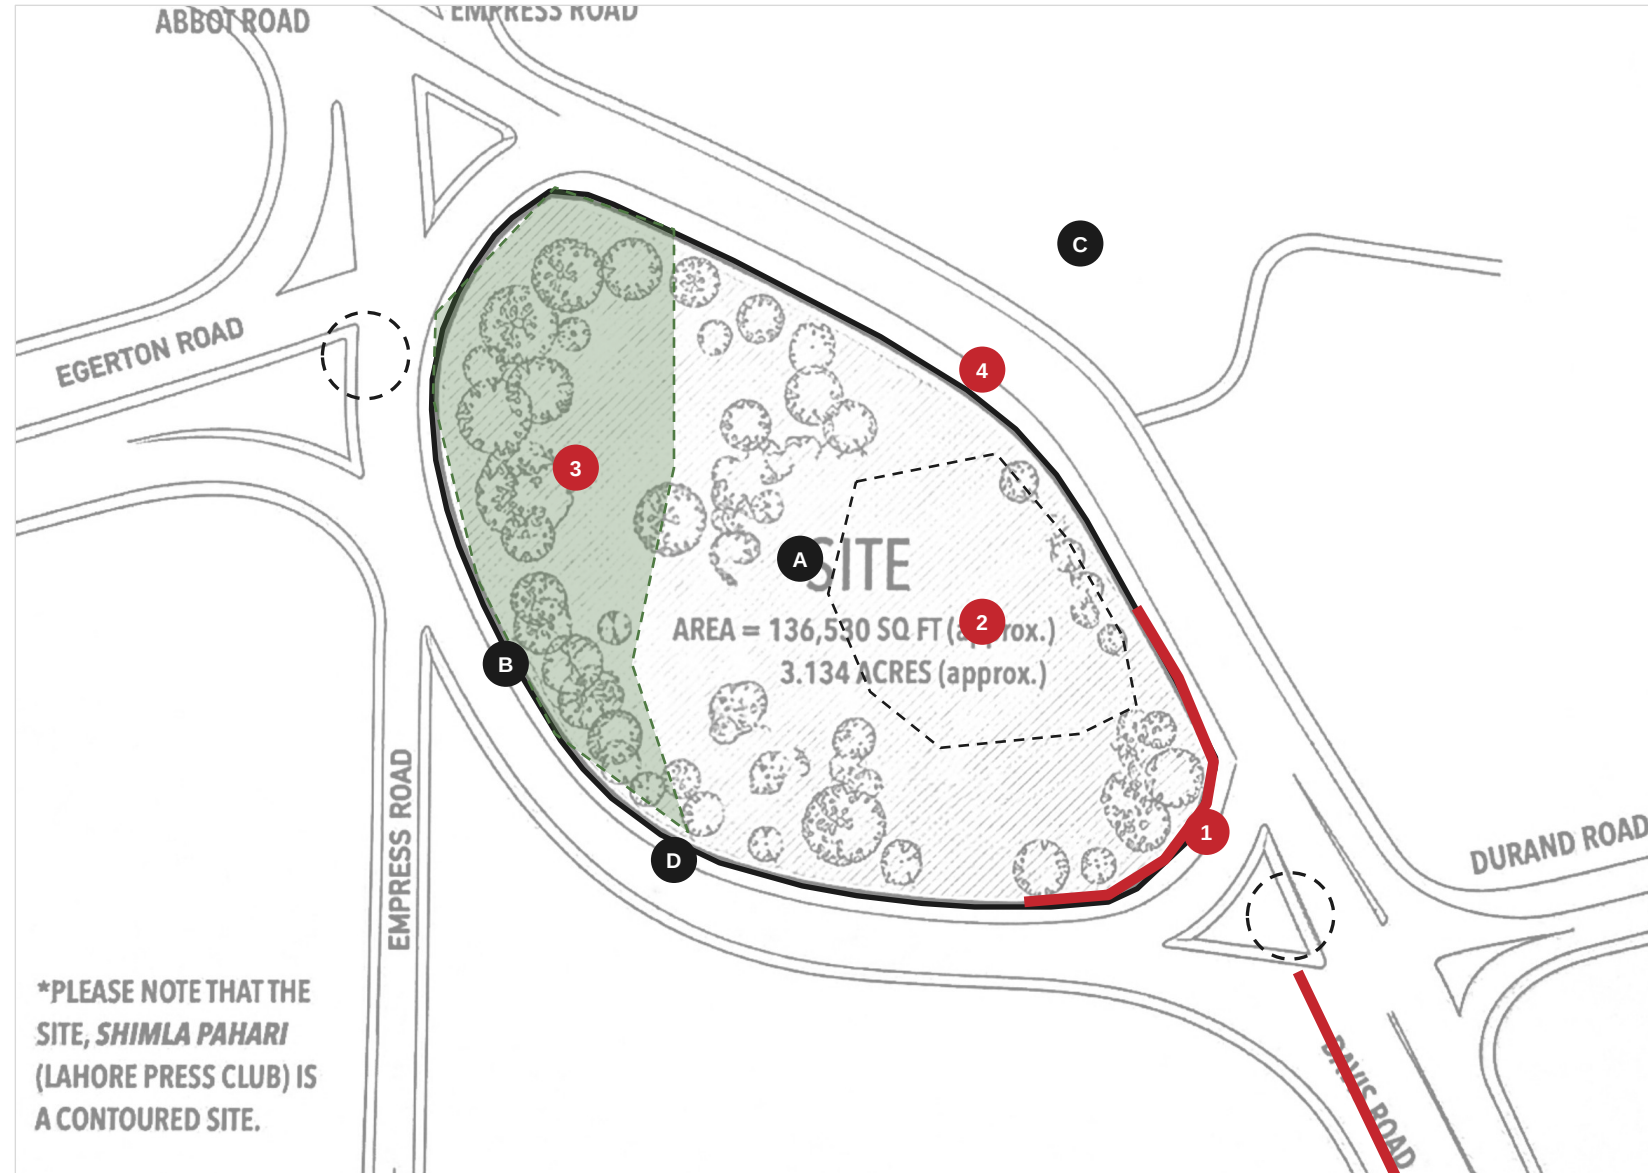

OPPORTUNITIES

- 1 SE tip faces the Davis / Durand junction: the handout's media street — the public, civic end.
- 2 Centre-east has the least tree cover as drawn: the most buildable ground.
- 3 Dense W-end trees: keep as a landscape the public can walk through.
- 4 NE long edge has a thin stretch of trees: possible service entry.

CONSTRAINTS


- A Topography must not be altered — levels unknown: building placement to be checked against a survey.
- B Tree ring along almost the whole perimeter: entries must thread between trees.
- C Roads on every side: all edges exposed to traffic (volumes not shown).
- D Press Club position unknown: zoning must stay flexible around it.

- opportunity (numbered)
- constraint (lettered)

PUBLIC / PRIVATE ZONING

03

Not a straight line: public at the SE edge AND an open top; working parts split to face the service edge.

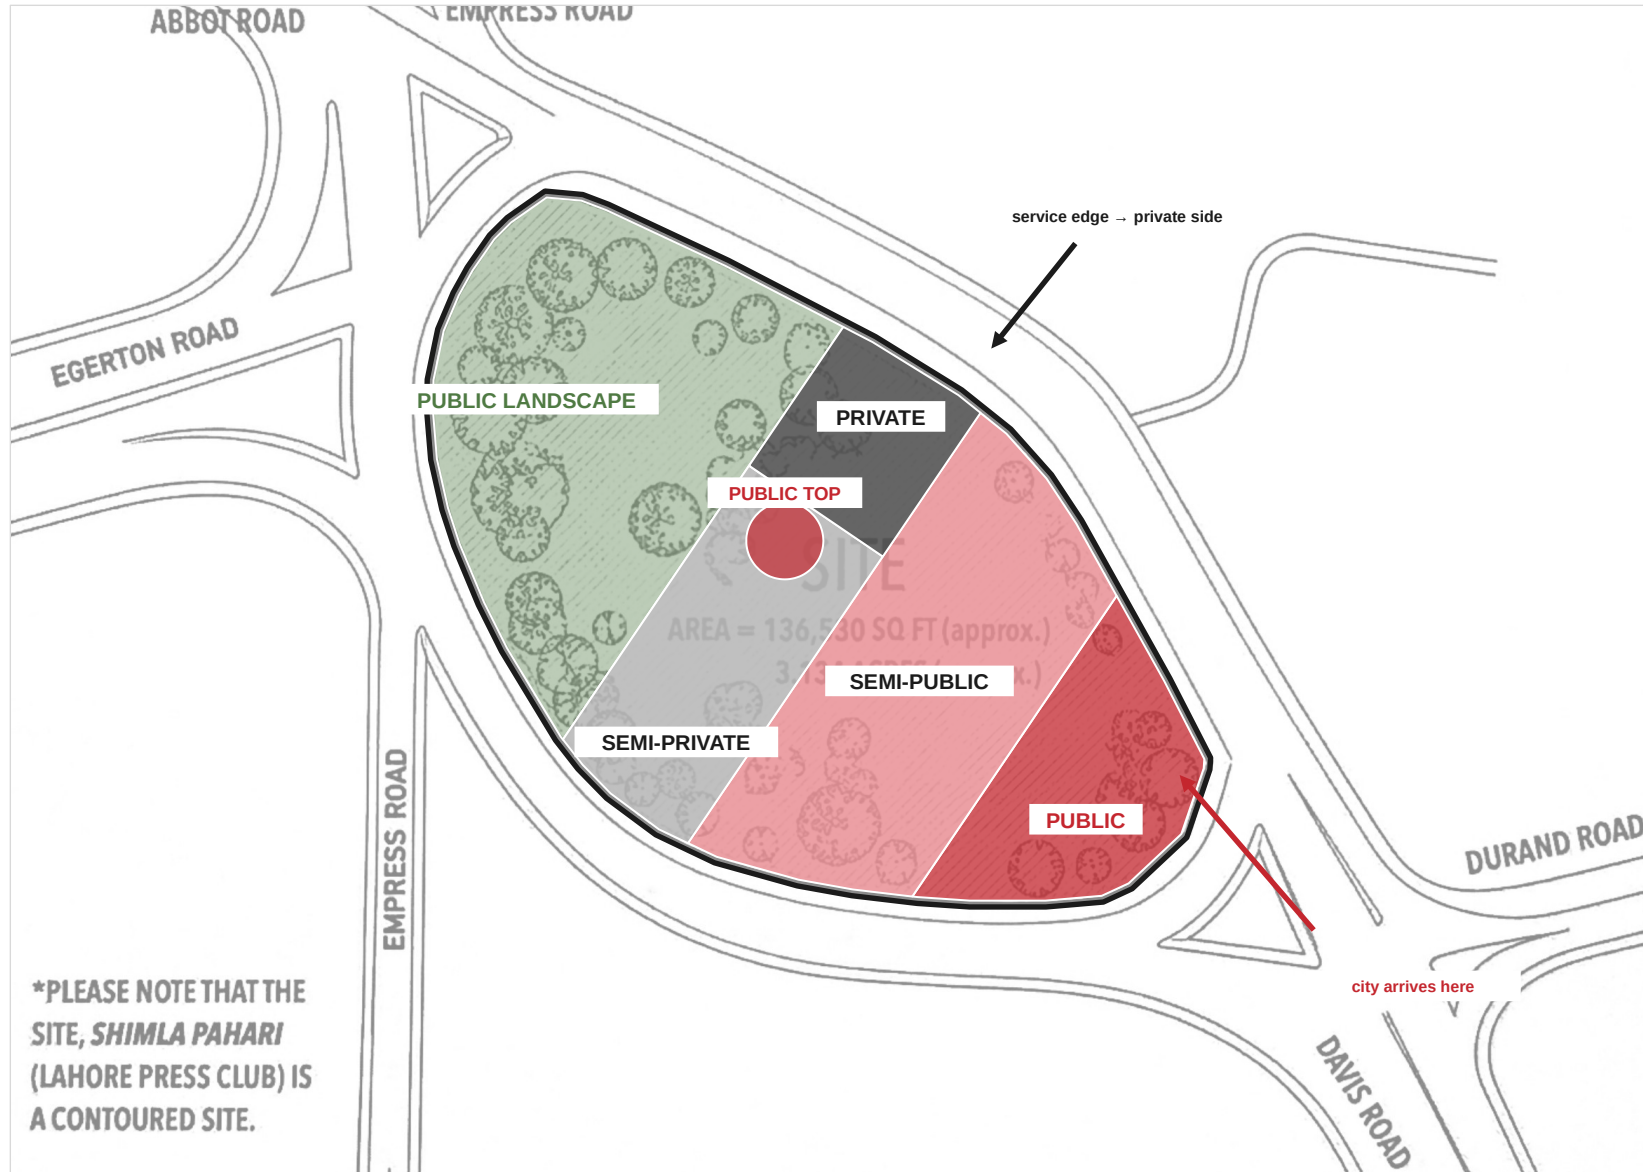

WHY EACH SITS WHERE IT DOES

Public the SE tip meets the junction and the media street — where crowds, cameras and speech already arrive.

Semi-public next ring in: reached through the public zone, never directly from the road.

Semi-private SW side of the centre, away from the service edge: research + archive reading.

Private NE side of the centre, next to the only thin tree stretch: loading reaches it without crossing public ground.


Public landscape + top the wooded W end and the open top stay public: the gradient reverses as you reach them.

- public
- semi-public
- semi-private
- private
- public landscape (preserved)

Gradient is my design interpretation; zone lines are diagrammatic, to be checked against levels + Press Club position.

PROGRAM ZONING

Large program clusters on the site — no rooms, no areas yet.

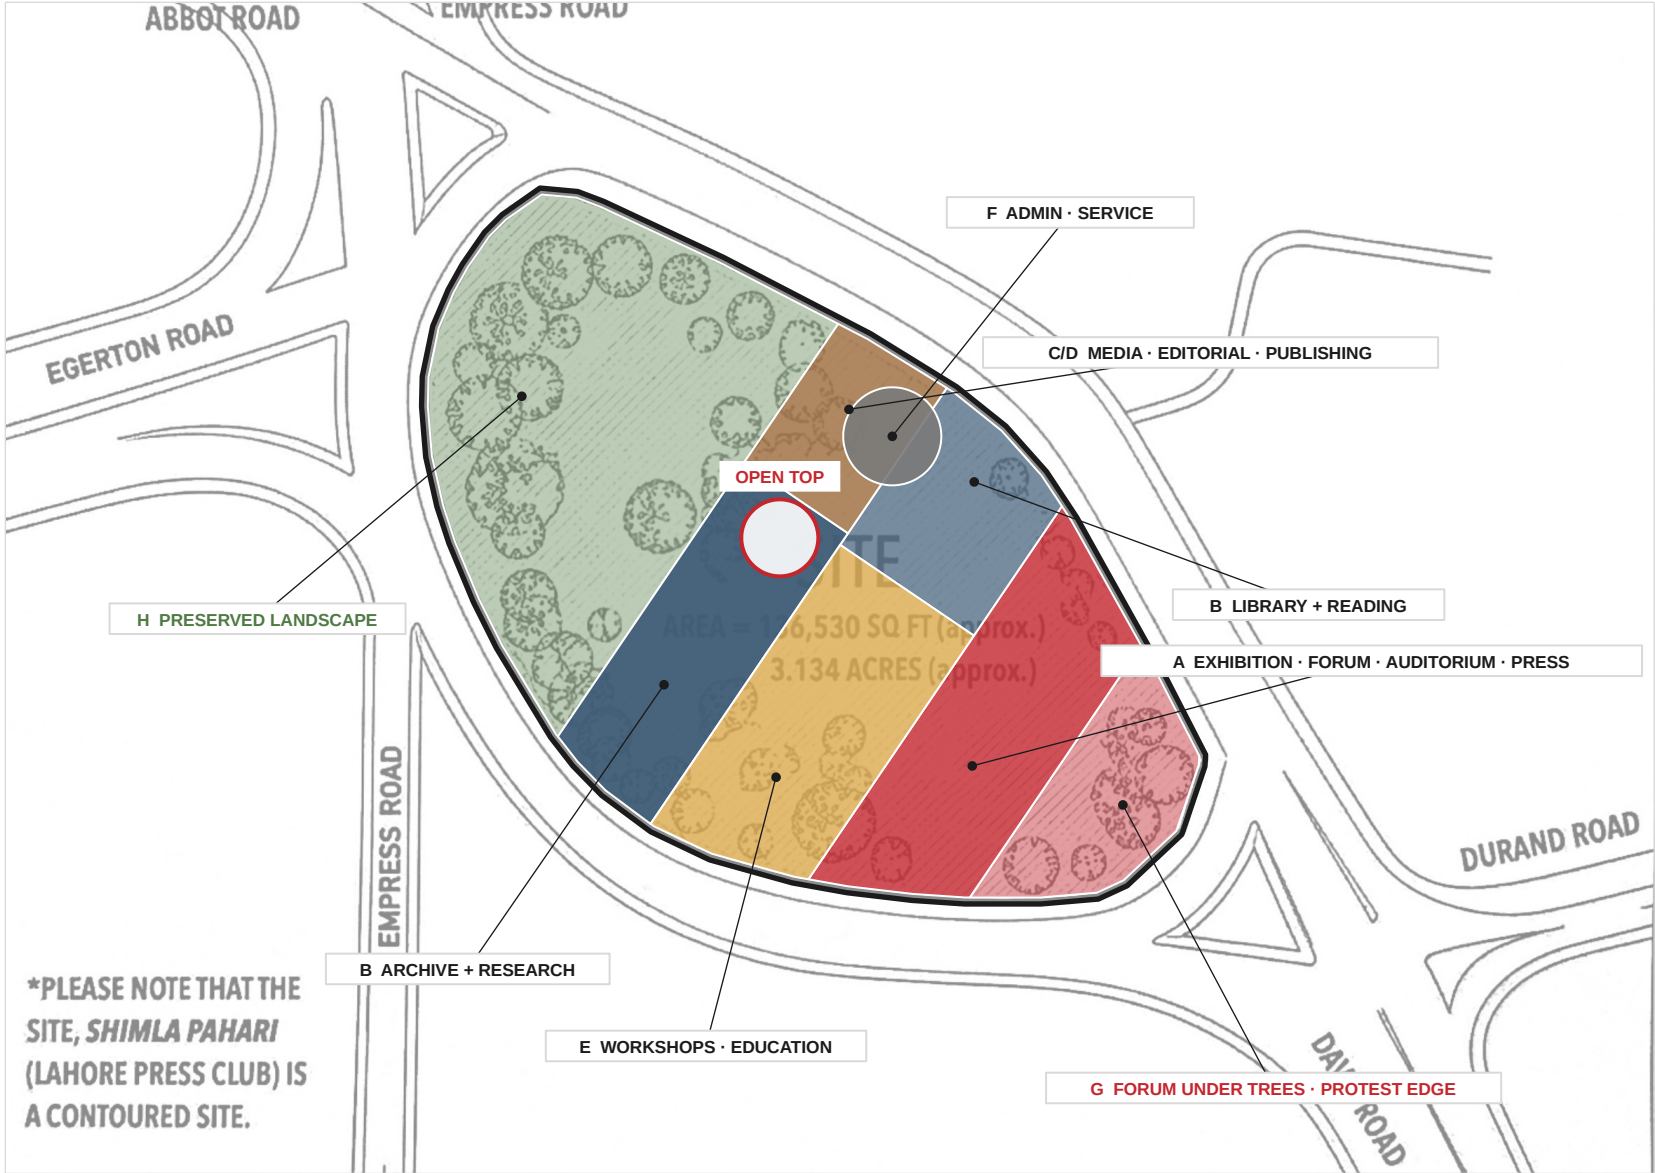

- A · G PUBLIC / CIVIC — forum, auditorium, exhibition, gathering
- B KNOWLEDGE — library, reading, archive, research
- C/D PRODUCTION — editorial, publishing, media
- E LEARNING — workshops, education
- F ADMIN / SERVICE
- H LANDSCAPE — preserved, walkable

READING ORDER (SE → NW)

- 1 road + junction → forum under trees (G)
- 2 civic halls facing it (A)
- 3 library + learning, side by side (B, E)
- 4 archive + research | media + publishing (B, C/D)
- 5 open top → wooded W end (H)

WHY THIS ORDER

Public program sits where the public already arrives; knowledge sits between the public and production so both reach it; production sits on the service edge; the most wooded ground stays unbuilt.

Program from handout: required = library + reading, archive, research + studios, media + recording, publishing. 'May include' = exhibition, forum, auditorium, workshops, education.

ACCESS + USER CIRCULATION

Three separate systems. Entry points are PROPOSED — existing gates are not shown on the plan.



- GENERAL PUBLIC — junction → forum → halls → library → open top
- - JOURNALISTS · RESEARCHERS · STAFF — own entry + route
- SERVICE / DELIVERY — NE edge only
- - public path through the wooded W end

CONFLICT POINTS → ZONING ANSWER

SE tip protest crowds + staff arriving together → staff get a second door off the SE route, beside the press room, not through the forum.

NE edge delivery vehicles cross the footpath → one short service bay only, next to production, trees kept either side.

Centre public route passes research → research on the SW side, route on the NE of it; windows, not doors, face the path.


RESTRICTED

archive stores · production floor · loading · admin

THREE ZONING OPTIONS

Same site, same program, three priorities. Not ranked.

A PUBLIC-CENTRIC

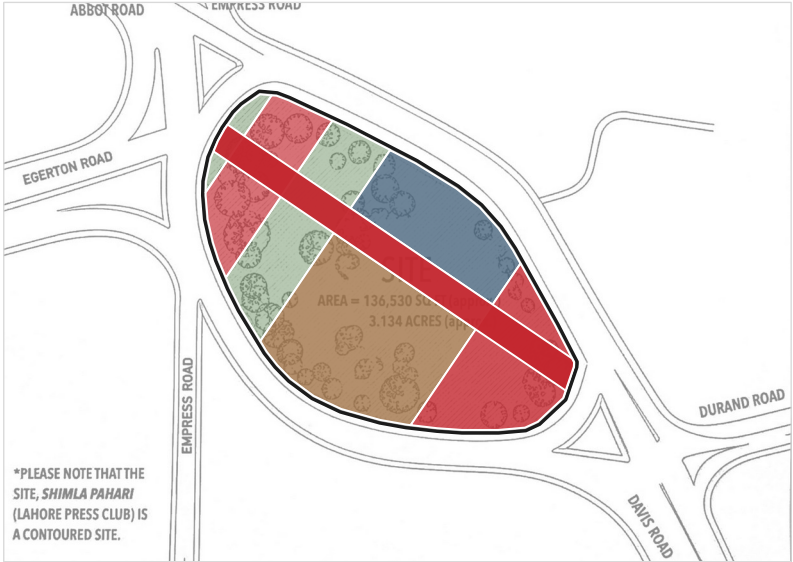


A public street crosses the whole site, junction to junction; civic halls at both ends.

+ strongest public presence; links both junctions · – cuts the wooded W end; production split by the street; many entries to secure

PRESS CLUB shares the SE civic end, or sits on the street
ROAD both junctions open
TOPOGRAPHY street must cross levels

B KNOWLEDGE / PRODUCTION

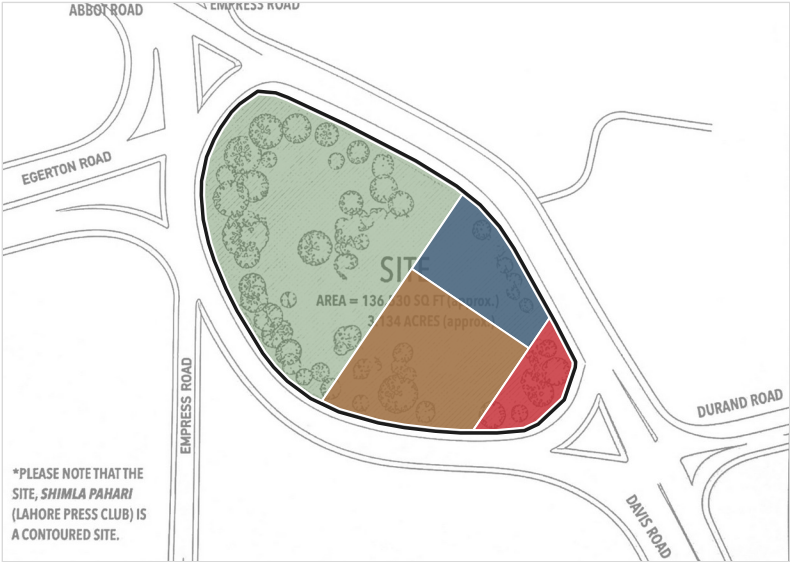


One compact knowledge + production core on the least-wooded ground; small public front at the SE tip.

+ efficient, easy to service and secure; smallest disturbance · – public limited to one edge; weakest civic engagement

PRESS CLUB stands as the core's public face
ROAD one public edge (SE)
TOPOGRAPHY built area smallest

C SITE / TOPOGRAPHY

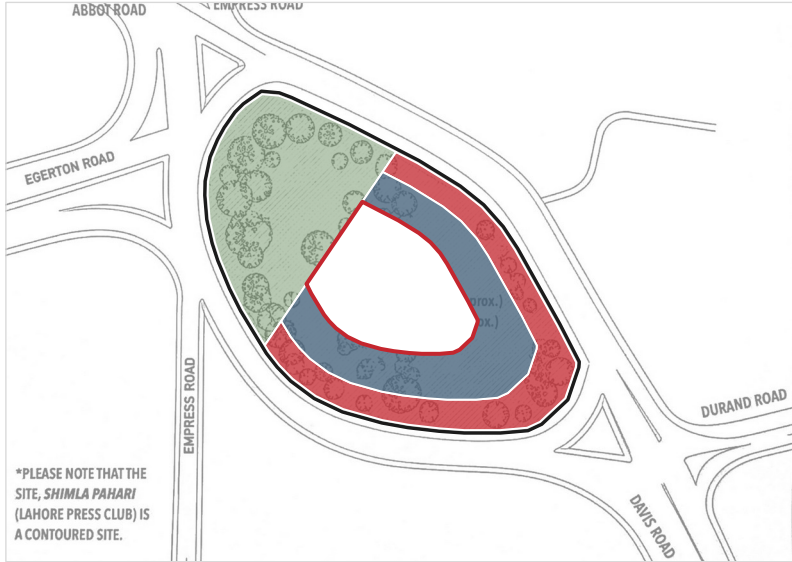

Rings follow the mound: public along the toe, knowledge mid-slope, open top; W end kept.

+ reads the mound; open top; route climbs · – depends on real levels (not on plan); ring along the toe faces traffic

PRESS CLUB joins the outer public ring
ROAD whole toe faces the road
TOPOGRAPHY zoning follows levels

- public / civic
- knowledge
- production
- landscape

The site plan illustrates the layout of the Shimla Pahari (Lahore Press Club) site, which is a contoured area of 3.134 acres (approx.) with a total area of 136,530 SQ FT (approx.). The site is bounded by Abbot Road to the north, Egerton Road to the west, Empress Road to the south, and Durand Road to the east. A central circular feature is labeled 'OPEN TOP'. The site is divided into several functional zones: F (Admin + Service), C/D (Media + Editorial + Publishing), B (Library + Reading), A (Exhibition + Forum + Auditorium + Press), G (Forum Under Trees + Protest Edge), E (Workshops + Education), and H (Preserved Landscape). A red dashed line indicates a boundary or path. A note at the bottom left states: '*PLEASE NOTE THAT THE SITE, SHIMLA PAHARI (LAHORE PRESS CLUB) IS A CONTOURED SITE.'

SITE public where the junction and media street are; building on the least-wooded ground; the W woods stay.

PROGRAM knowledge in the middle, reachable from both the public and the working side.

USERS three separate entries; they meet in the forum, library and on the route.

VISION the public reaches the top of the landmark; production is next to the route, not hidden.

TOPOGRAPHY zones follow the mound in plan; no flattening. Levels to be surveyed.

If near the SE tip keep it; it becomes the press face of the civic zone A, sharing the forum G.

If mid-site keep it; the public route passes it; link at ground level.

If in the W woods keep it as a pavilion in the landscape; connect by path.

- public / civic
knowledge
production
learning
landscape
- public
staff
service


SITE ZONING — SHIMLA PAHARI

SITE → CONDITIONS → OPPORTUNITIES / CONSTRAINTS → ACCESS → USERS → PROGRAM → OPTIONS → FINAL


01 SITE CONDITIONS




02 PUBLIC / PRIVATE

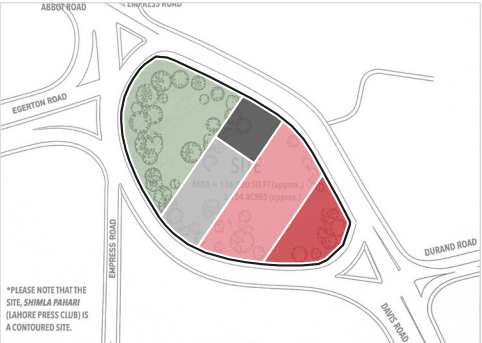


03 ACCESS + USERS

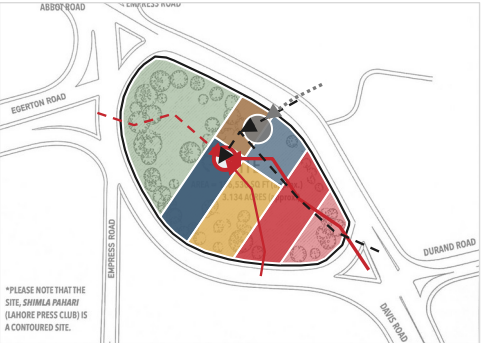


07 FINAL ZONING

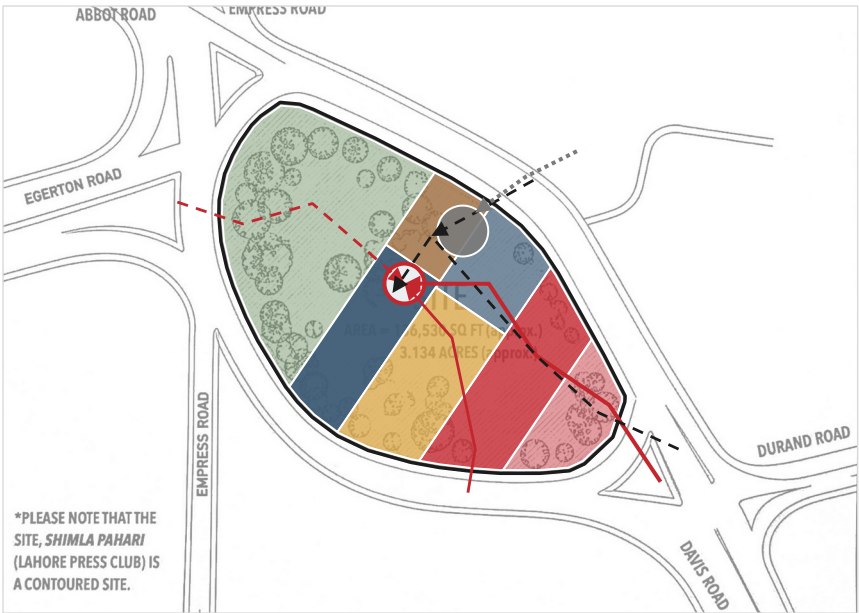

04 OPTION A

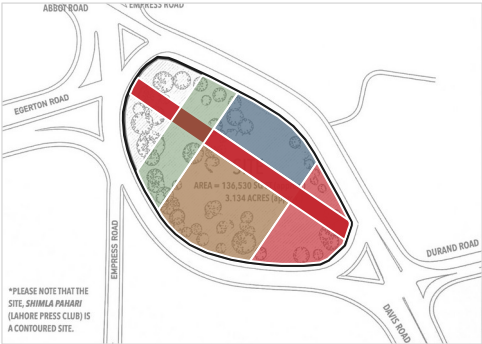

05 OPTION B

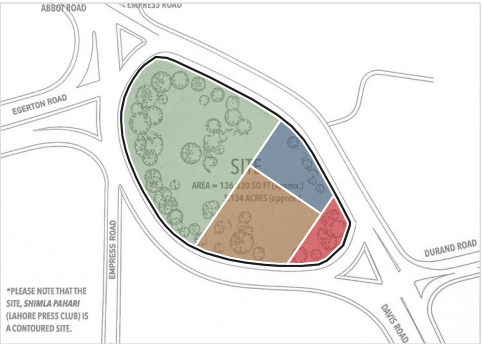

06 OPTION C



- public / civic
- knowledge
- production
- learning
- landscape
- public
- staff
- service

Public where the city arrives · knowledge in the middle · production on the service edge · woods and top stay open.

Base: handout site plan (p.4). Press Club footprint, levels and existing gates are not shown on it and must be added from a survey.