

GROUND FLOOR PLAN — WHOLE SITE

The Contemporary Publishing House · Shimla Pahari, Lahore



feet · north not shown on survey


KEY

- poché / wall
- glazing (thin double line)
- timber floor
- tiled (wet areas)
- paving / forum
- planted slope

①②③ / (A) (B) structural grid per building
FFL finished floor level above the survey ±0'-0" at the entrance
Areas ft², measured off the drawing (proposal)

Base: Shimla Pahari survey (contours, levels, dimensions). Old Press Club removed. Building sizes, rooms, furniture and service access are design proposals.



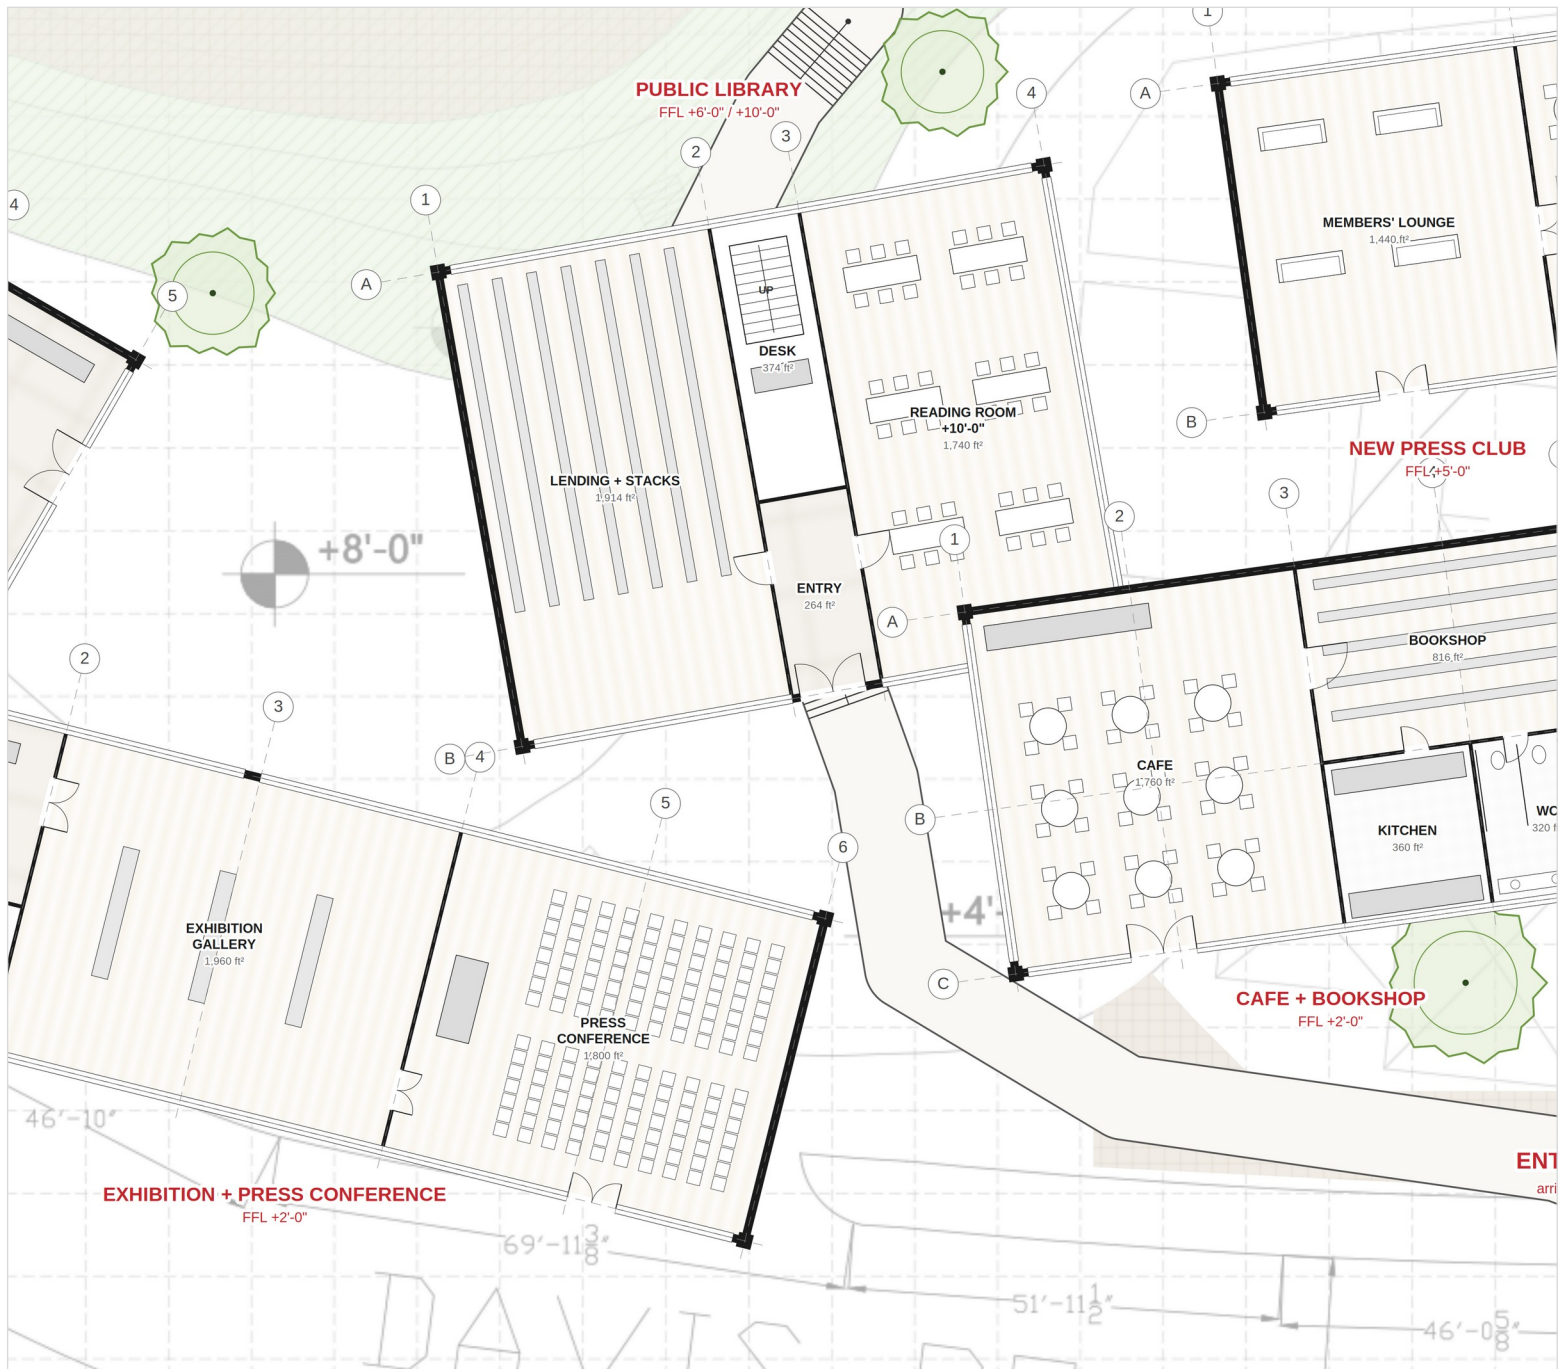

ENLARGED PLAN 1 — CIVIC FRONT: exhibition · press conference · library · cafe

The Contemporary Publishing House · Shimla Pahari, Lahore



feet · north not shown on survey

KEY

- poché / wall
- glazing (thin double line)
- timber floor
- tiled (wet areas)
- paving / forum
- planted slope

①②③ / (A) (B) structural grid per building
 FFL finished floor level above the survey ±0'-0" at the entrance
 Areas ft², measured off the drawing (proposal)

Base: Shimla Pahari survey (contours, levels, dimensions). Old Press Club removed. Building sizes, rooms, furniture and service access are design proposals.



ENLARGED PLAN 2 — CLUB + RECREATION: new press club · games · admin · workshops · court

The Contemporary Publishing House · Shimla Pahari, Lahore



feet · north not shown on survey

KEY


- poché / wall
- glazing (thin double line)
- timber floor
- tiled (wet areas)
- paving / forum
- planted slope

①②③ / (A) (B) structural grid per building

FFL finished floor level above the survey ±0'-0" at the entrance


Areas ft², measured off the drawing (proposal)

Base: Shimla Pahari survey (contours, levels, dimensions). Old Press Club removed. Building sizes, rooms, furniture and service access are design proposals.

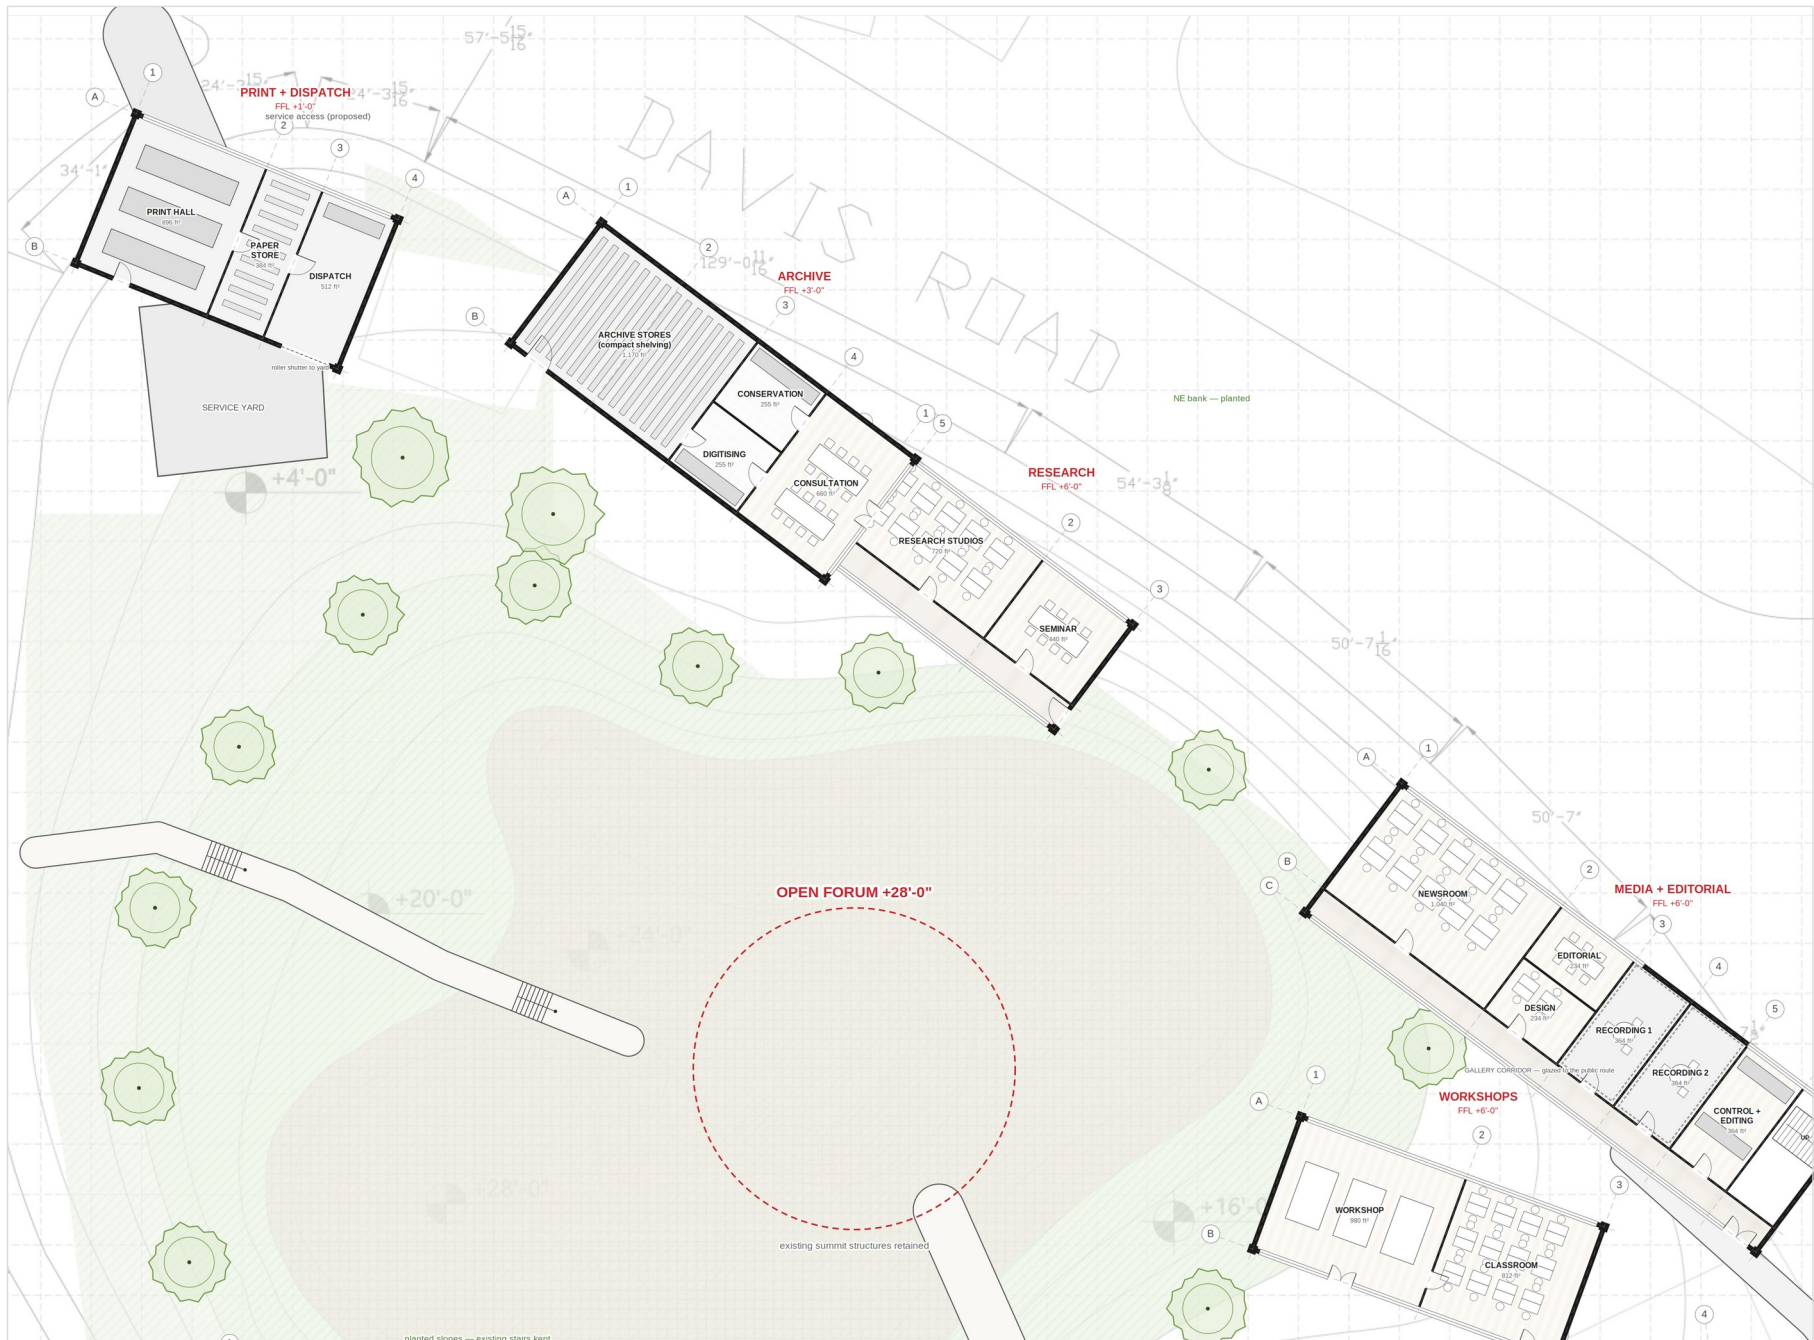

ENLARGED PLAN 3 — NE BANK: print · archive · research · media + editorial

The Contemporary Publishing House · Shimla Pahari, Lahore

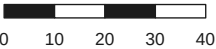

feet · north not shown on survey

KEY

- poché / wall
- glazing (thin double line)
- timber floor
- tiled (wet areas)
- paving / forum
- planted slope

① ② ③ / (A) (B) structural grid per building

FFL finished floor level above the survey ±0'-0" at the entrance

Areas ft², measured off the drawing (proposal)

Base: Shimla Pahari survey (contours, levels, dimensions). Old Press Club removed. Building sizes, rooms, furniture and service access are design proposals.